

Trapp: Kort rett trapp (8 trinn)

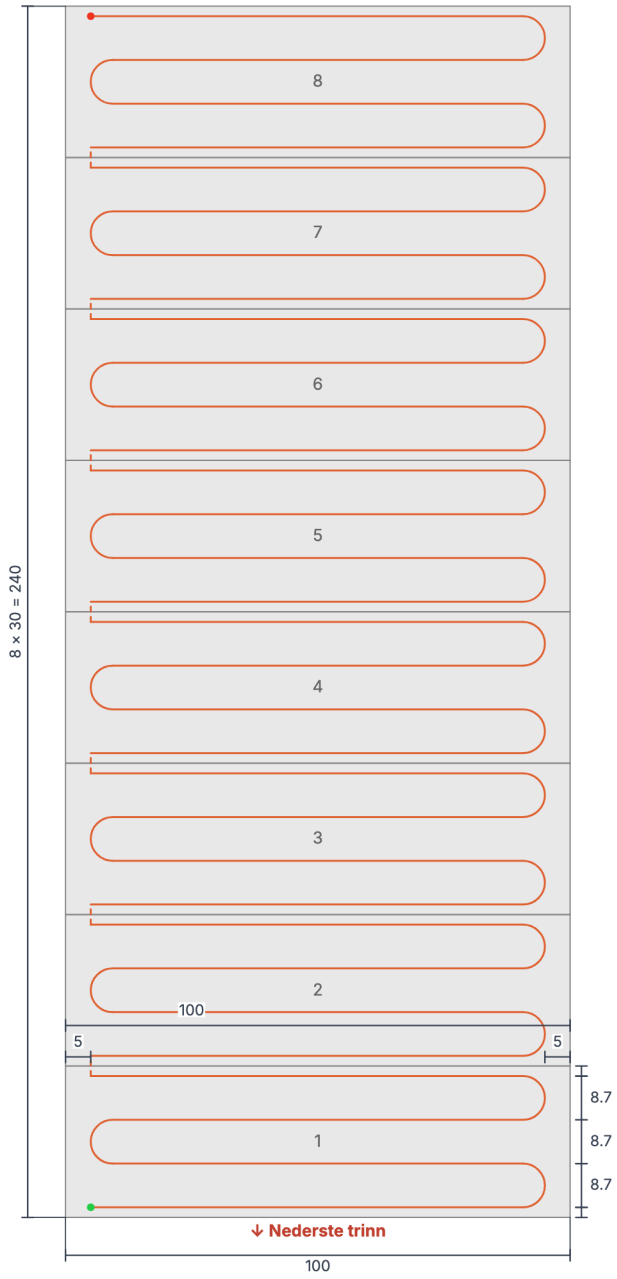

Start kabel Slutt kabel

Målestokk 1:15 (A4)

Sidevisning

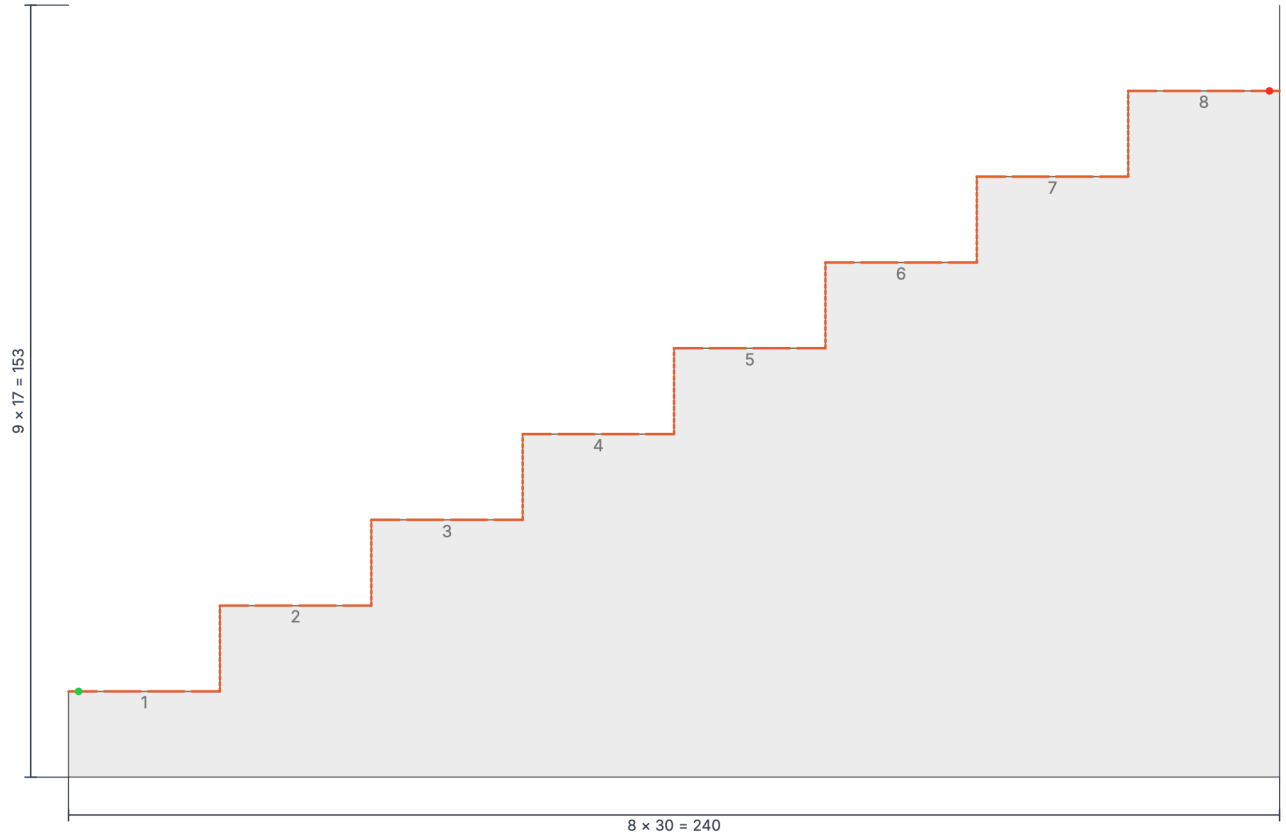

Målestokk 1:15 (A4)

Kabel per flate

Flate	Strenger	CC	Kabel (m)
Trinn 1–8 (typisk)	4	8.7 cm	3.6 per trinn

K1

0 W

—

Avstand opptrinn: 2 cm | Avstand nese: 2 cm | Avstand sider: 5 cm
4 strenger/trinn | CC 8.7 cm | 90 cm/streng | 360 cm/trinn | —
Trinn: 28.8 m | Repos: — | Lagt: 30.3 m | Kabellengde: —

Totalt: 30.3 m | 0 W

Samlet kabel: 0.0 m